


Bulkhead Wall

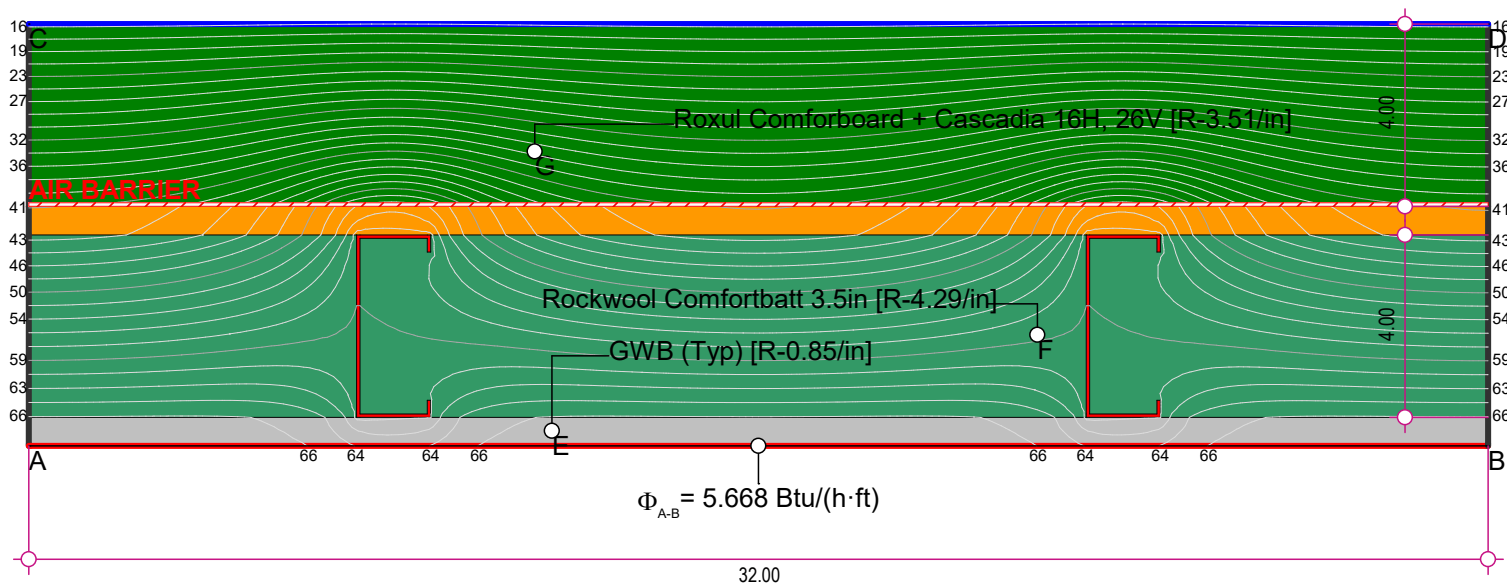

$$U_{eq\ A-B} = \frac{5.668}{54.0 \cdot 2.667} = 0.0394\ Btu/(h \cdot ft^2 \cdot F) = R\ 25.4$$

Boundary Condition				Material		$\lambda[Btu/(h \cdot ft \cdot F)]$		ϵ
$q[Btu/(h \cdot ft^2)]$	$\theta[^\circ F]$	$h[Btu/(h \cdot ft^2 \cdot F)]$	ϵ					
Exterior, ventilated	14.000	1.355		GWB (Densglas Sheathing)[R-1.12/in]		0.074	0.900	
Interior, normal, horizontal	68.000	1.355		GWB (Typ) [R-0.85/in]		0.098	0.900	
Symmetry/Model section	0.000			Rockwool Comfortbatt 3.5in [R-4.29/in]		0.019	0.900	
				Roxul Comforboard + Cascadia 16H, 26V [R-3.51/in]		0.024	0.900	
				Steel (Plain Carbon) [R-0.0024/in]		34.956	0.900	