


Cellar Floor

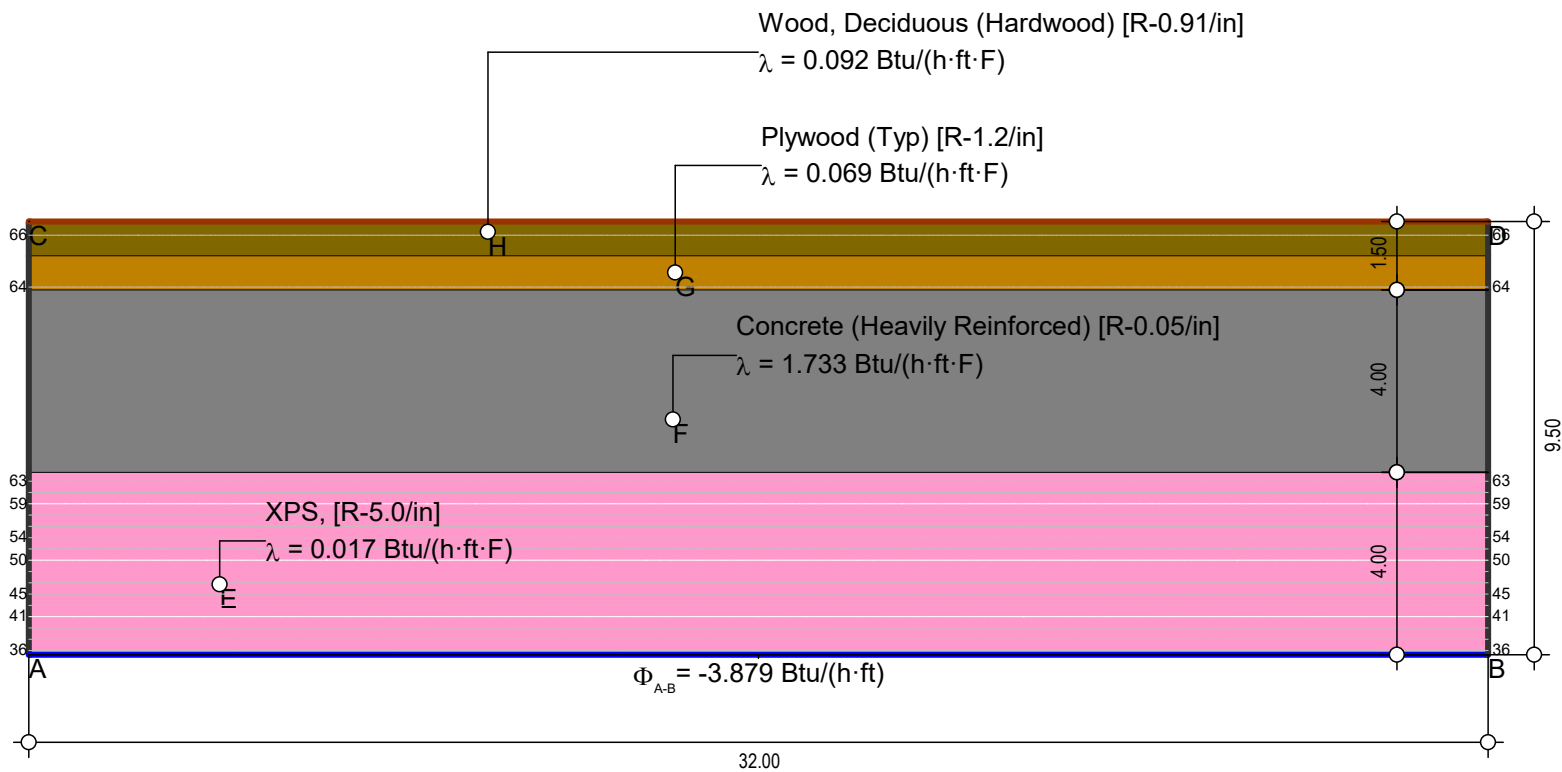

$$U_{eq \text{ A-B}} = \frac{3.879}{33.408 \cdot 2.667} = 0.0435 \text{ Btu}/(\text{h}\cdot\text{ft}^2\cdot\text{F}) = R-23.0$$

Boundary Condition	q[Btu/(h·ft²)]	θ[F]	h[Btu/(h·ft²·F)]	ε	Material	λ[Btu/(h·ft·F)]
Exterior, NYC 90d Avg		34.592	4.403		Concrete (Heavily Reinforced) [R-0.05/in]	1.733
Interior, heat flux, downwards		68.000	1.036		Plywood (Typ) [R-1.2/in]	0.069
Symmetry/Model section	0.000				Wood, Deciduous (Hardwood) [R-0.91/in]	0.092
					XPS, [R-5.0/in]	0.017