


Party Wall

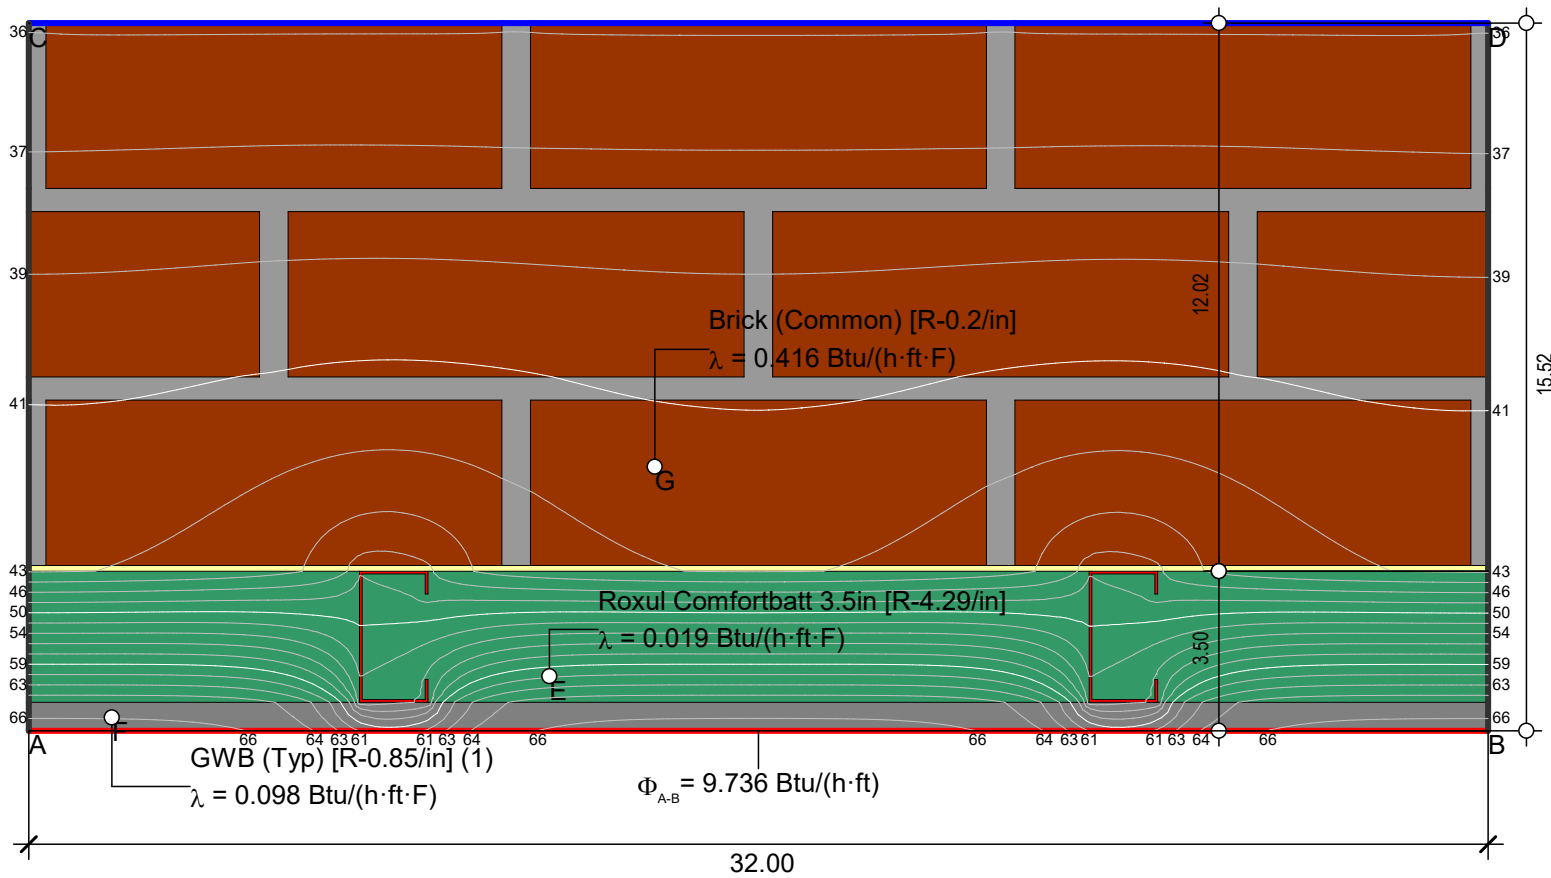

$$U_{eq\ A-B} = \frac{9.736}{33.408 \cdot 2.667} = 0.109\ Btu/(h \cdot ft^2 \cdot F) = R-9.17431$$

Boundary Condition					Material	$\lambda[Btu/(h \cdot ft \cdot F)]$
$q[Btu/(h \cdot ft^2)]$	$\theta[F]$	$h[Btu/(h \cdot ft^2 \cdot F)]$	ϵ			
Exterior, NYC 90d Avg	34.592	4.403	0.098		Brick (Common) [R-0.2/in]	0.416
Interior, normal, horizontal	68.000	1.355	0.000		GWB (Typ) [R-0.85/in] (1)	0.098
Symmetry/Model section	0.000				Mortar - Portland Cement-Lime (PHI)	0.520
					Roxul Comfortbatt 3.5in [R-4.29/in]	0.019
					Steel (Rolled, Ground) [R-0.0029/in]	28.889
					Stucco [R-0.2/in]	0.417